
# LIGHTING FIXTURE LIST

| | |
|---|---|
| A | SURFACE DRUM, OPAL LENS, 1500 LUM LED, 15VA, 120V |
| B | WALL SCONCE, CIRCULAR, OPAL LENS, 1000 LUM LED, 10VA, 120V |
| C | Downlight – 6" Recessed Incandescent, 120 V |
| D | Pendant Light – Disk, 100 W, 120 V |
| E | Sconce Light - Uplight 60W - 120V |
| F | Strip Light – 4', 120 V |
| G | Sconce Light - Uplight 60W - 120V |
| H | Downlight - Under Cabinet 120V (1' 6") |
| H1 | Downlight - Under Cabinet 120V (2') |

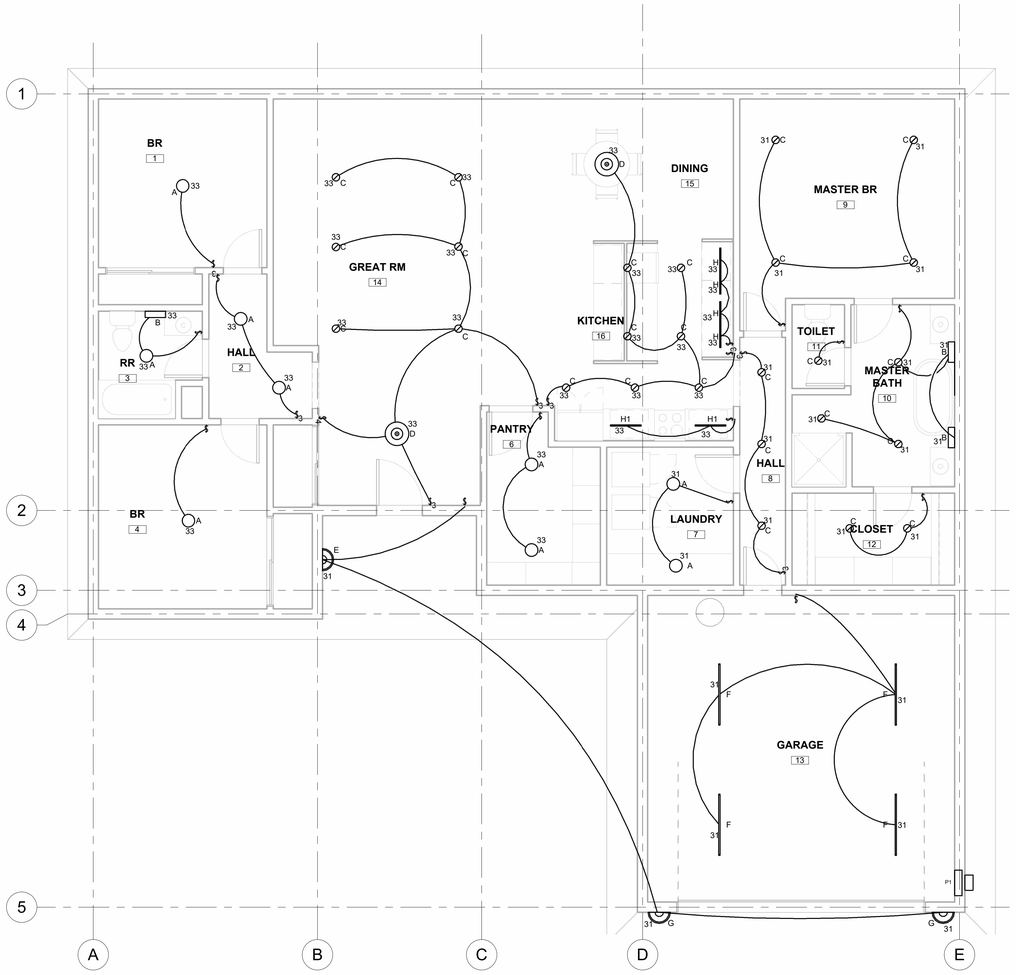


PROJECT NORTH

1 FLOOR PLAN - LIGHTING
1/4" = 1'-0"

AUTODESK

www.autodesk.com/revit

Consultant
Address
Address
Address
Phone

Consultant
Address
Address
Address
Phone

Consultant
Address
Address
Address
Phone

Consultant
Address
Address
Address
Phone

Consultant
Address
Address
Address
Phone

| No. | Description | Date |
|---|---|---|
| | | |

# PROJECT

3-BEDROOM HOME

## FLOOR PLAN - LIGHTING

| | |
|---|---|
| Project Number | EE-001 |
| Date | 10/14/2026 |
| Drawn By | JOHN MARK |
| Checked By | N/A |

# E201

| | |
|---|---|
| Scale | As indicated |

10/15/2026 10:04:39 AM