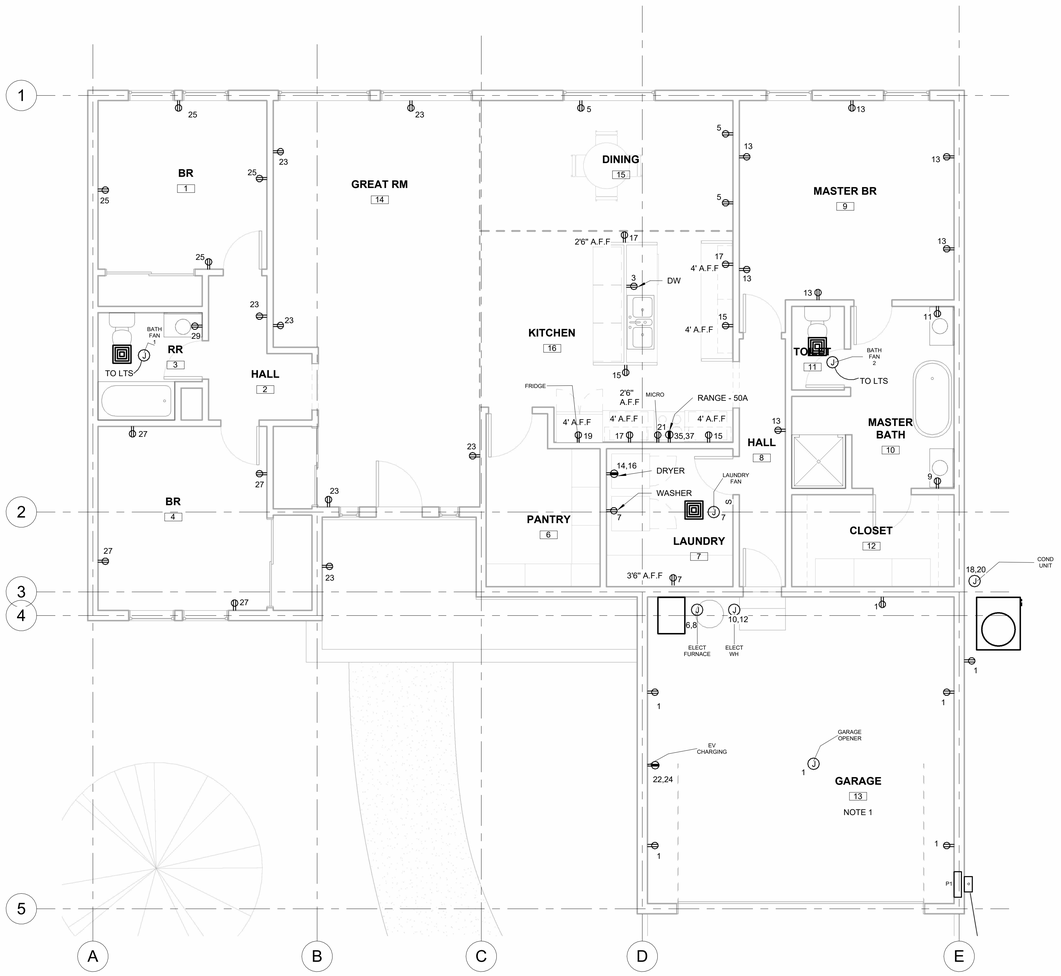


1 FLOOR PLAN - POWER
1/4" = 1'-0"

PROJECT NORTH

POWER PLAN KEYED NOTES

1. ALL RECEPTACLES IN GARAGE TO BE AT +48" ABOVE FINISHED FLOOR.

AUTODESK

www.autodesk.com/revit

Consultant
Address
Address
Address
Phone

Consultant
Address
Address
Address
Phone

Consultant
Address
Address
Address
Phone

Consultant
Address
Address
Address
Phone

Consultant
Address
Address
Address
Phone

No.	Description	Date

PROJECT

3-BEDROOM HOME

FLOOR PLAN - POWER

Project Number	EE-001
Date	10/14/2026
Drawn By	JOHN MARK
Checked By	N/A

E301

Scale: As indicated

10/15/2026 10:06:08 AM