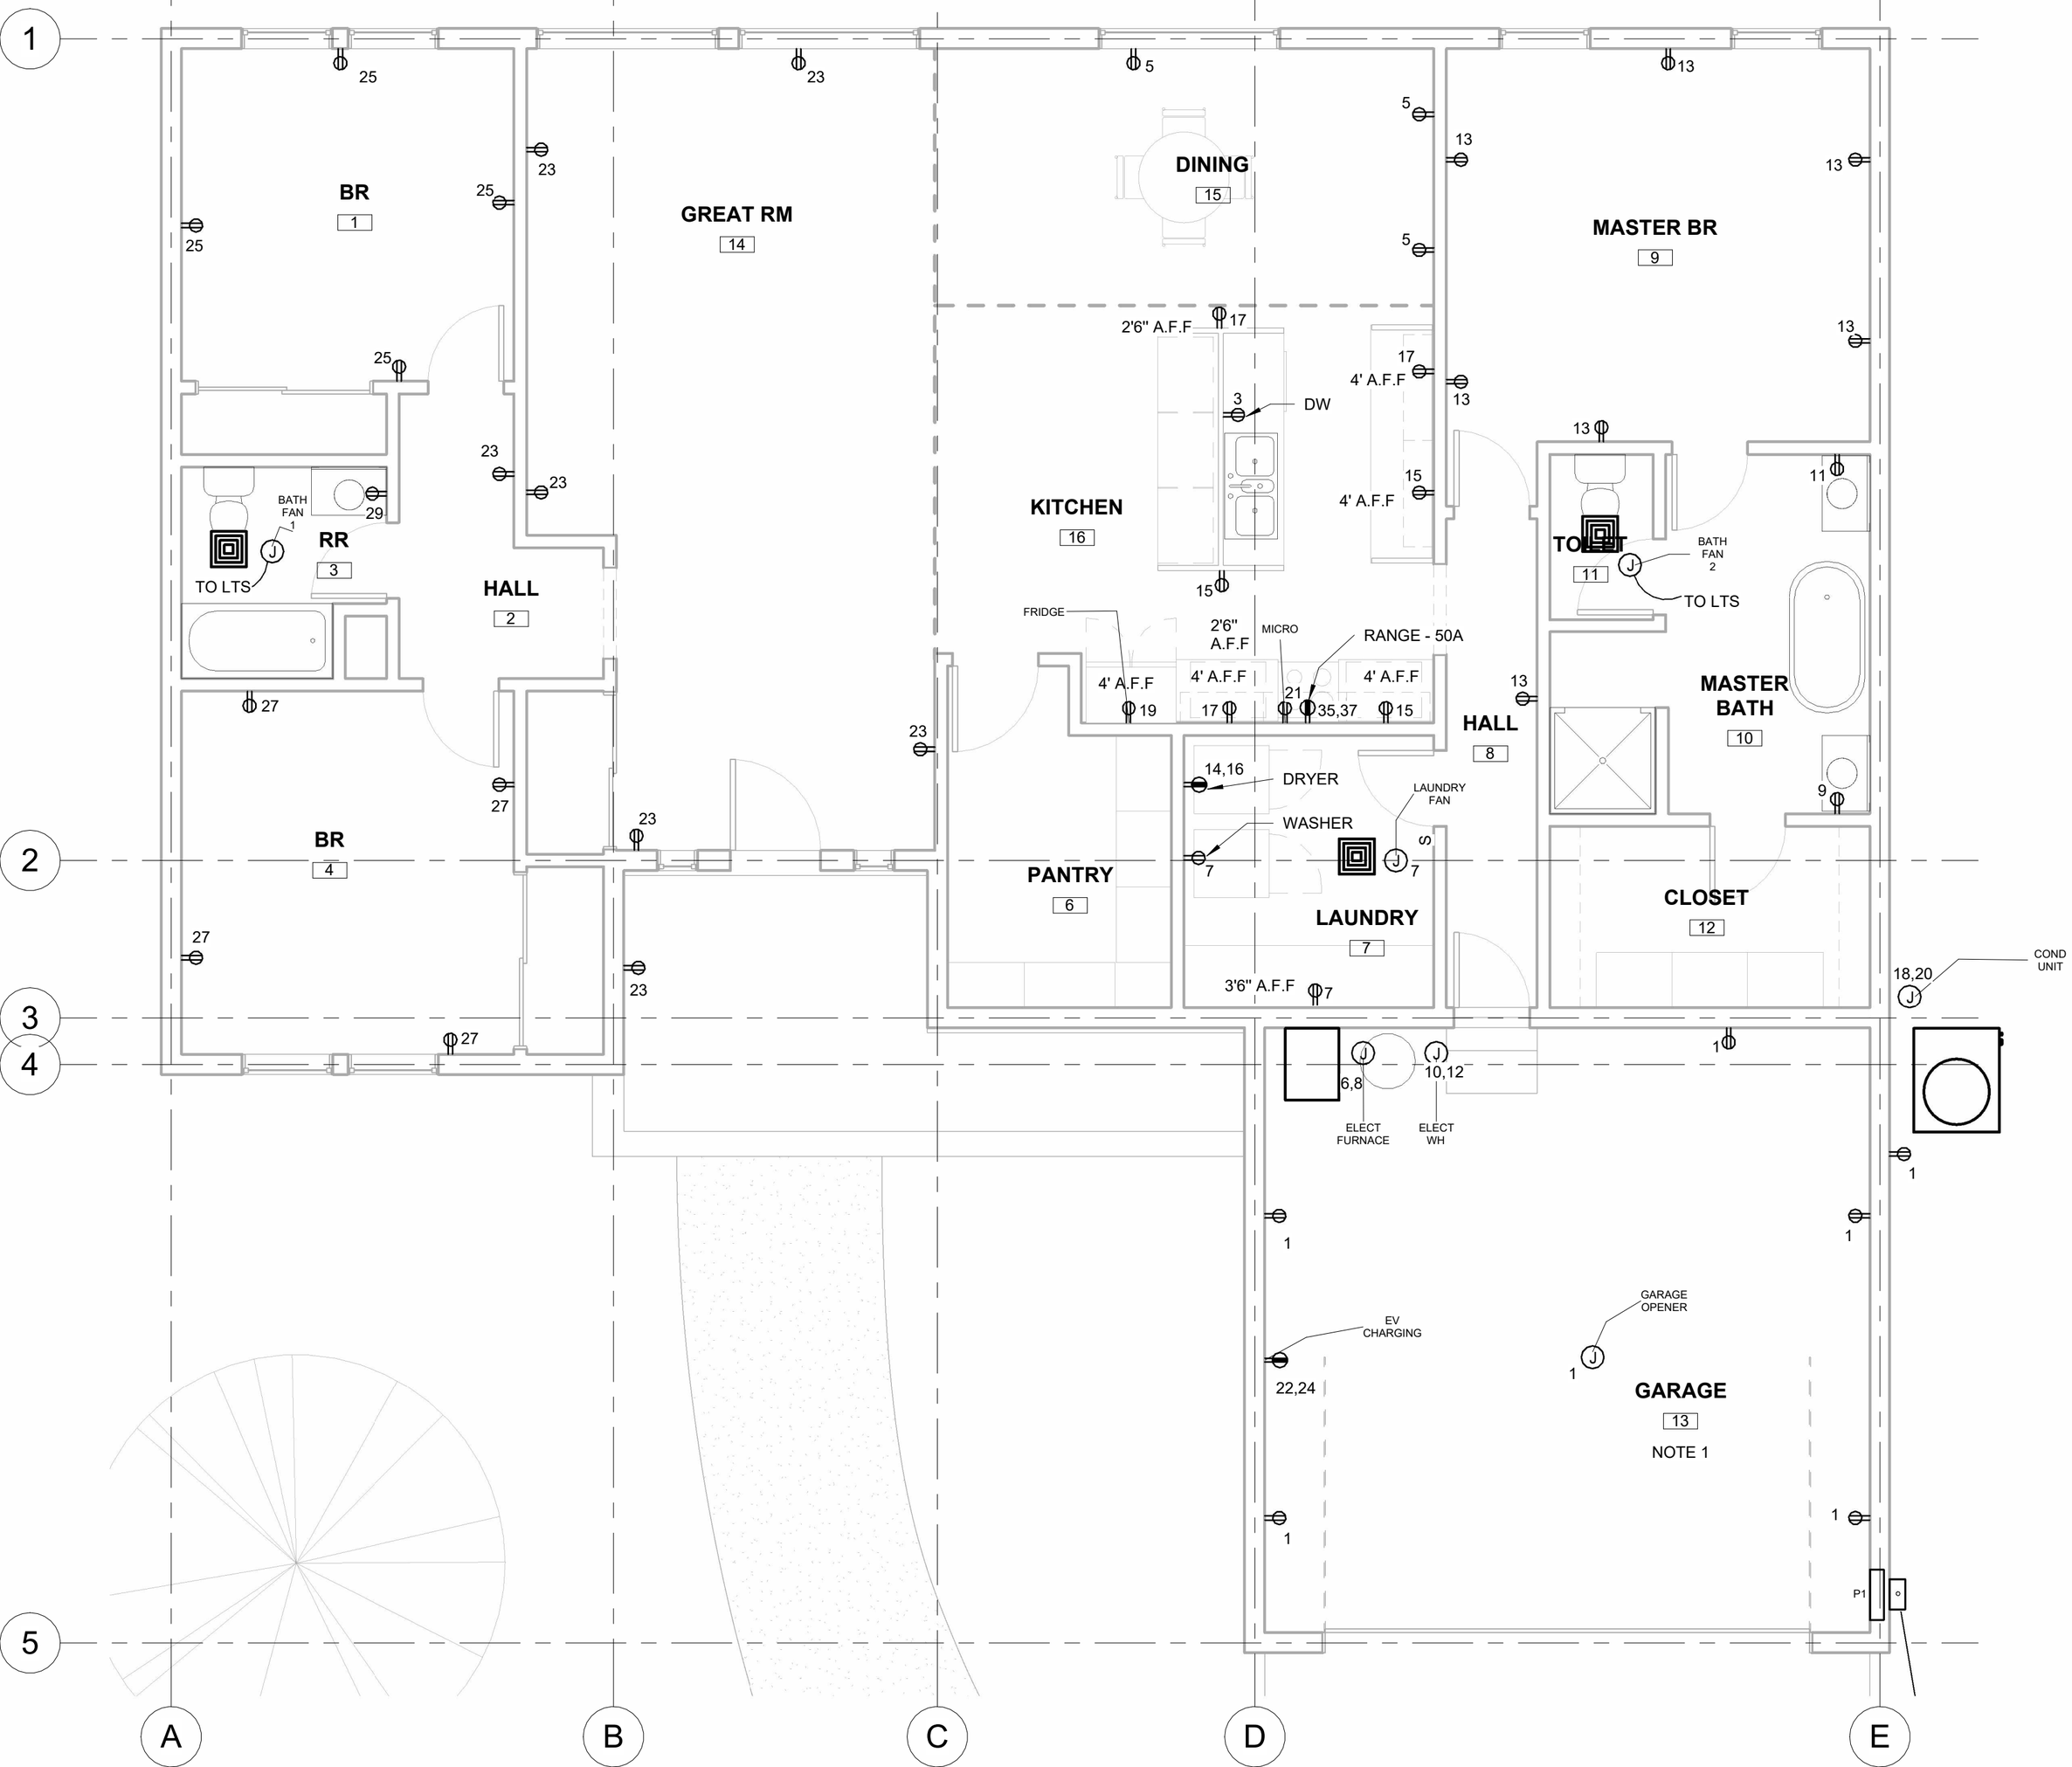

BR
1
GREAT RM
14
DINING
15
MASTER BR
9
KITCHEN
16
RR
3
HALL
2
TOILET
11
MASTER BATH
10
HALL
8
BR
4
PANTRY
6
LAUNDRY
7
CLOSET
12
GARAGE
13
NOTE 1
BATH FAN 1
TO LTS
BATH FAN 2
TO LTS
2'6" A.F.F
DW
4' A.F.F
FRIDGE
2'6" A.F.F
MICRO
RANGE - 50A
4' A.F.F
4' A.F.F
4' A.F.F
DRYER
WASHER
LAUNDRY FAN
3'6" A.F.F
COND UNIT
ELECT FURNACE
ELECT WH
EV CHARGING
GARAGE OPENER
P1
A
B
C
D
E
1
2
3
4
5